

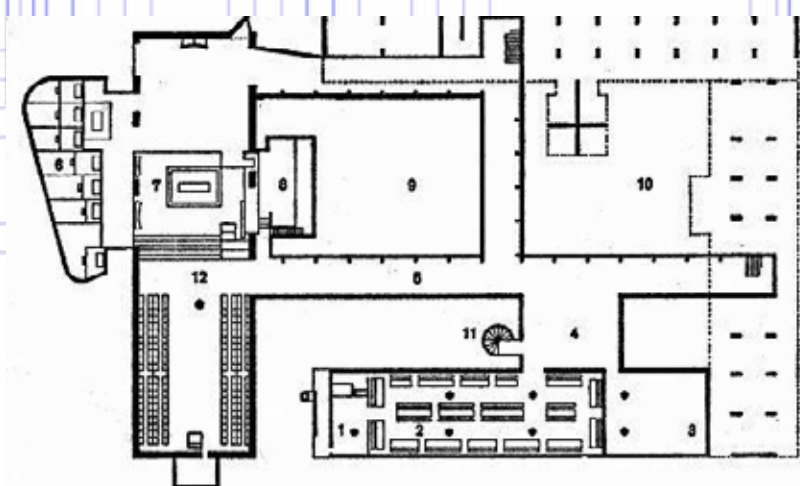
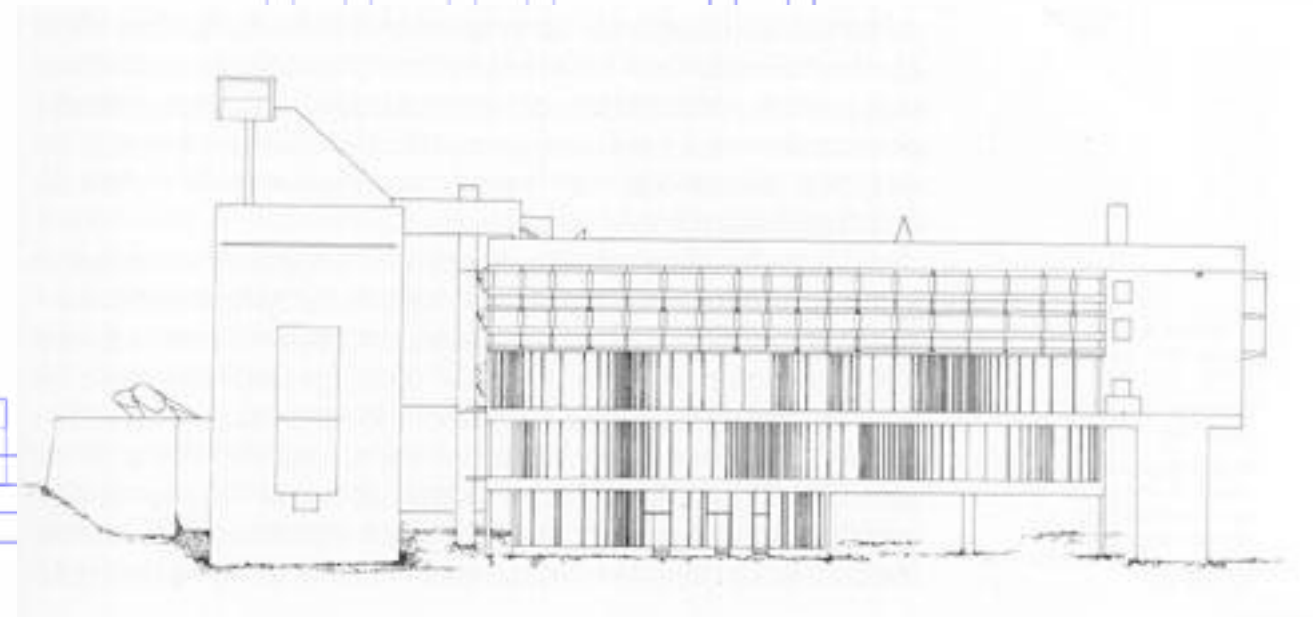


SAINTE MARIE DE LA TOURETTE BY
LE CORBUSIER AND IANNIS XENAKIS.

A Dominican Order priory, located on a hillside near Lyon, France designed by the architect Le Corbusier, the architect's final and most important building. The design of the building begun in May 1953 and completed in 1961. The committee that decided the creation of the building, considered that the primary duty of the monastery should be the spiritual awakening of the people and in particular the inhabitants of nearby areas.

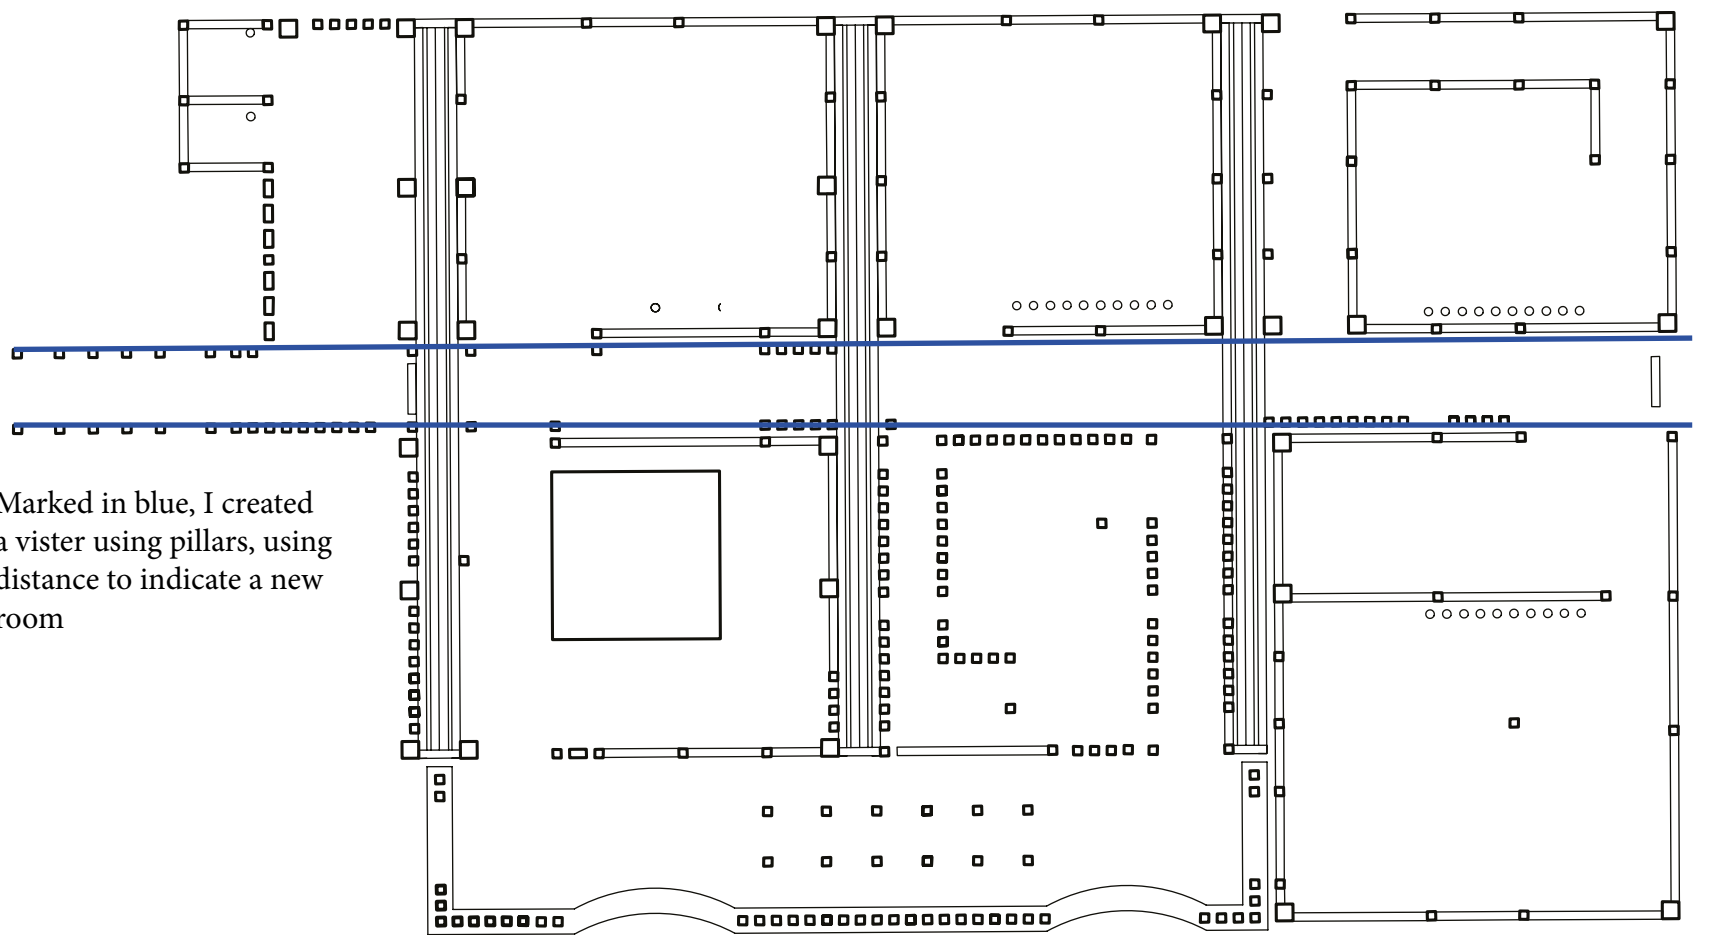

Refectory floor
1 Pantry, 2 Refectory, 3 Chapter-room, 4 Atrium, 5 Cloister, 6 Lower church, 7 High altar, 8 Sacristy, 9, 10 Courtyard, 11 Spiral staircase.

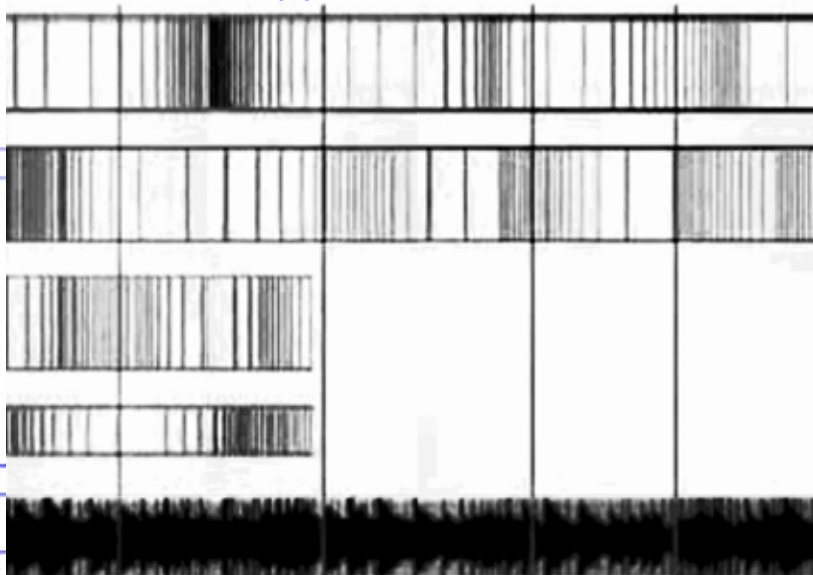

Marked in blue, I created a vister using pillars, using distance to indicate a new room