

Back to Basics

Back to times of the past. An off-grid urban village that operates for and with the people of Hackney wick. This housing unit serving a 35sqm living space is a solution to many problems.

New developments are leading to the disappearance of those who created it, the local community who are now seeking new jobs and homes, leading to a division between old and new comers. The proposed living unit provides an alternative to low cost housing which serves as a way to live with a reduction to ones cost of living. Systems built for and around the unit create the ability to live completely off the grid from public services. Storage energy for weathering days and environmental strategies proposed to create passive-house design outcomes. Environmental analysis work was completed to allow for a practical understanding to the matter with the passive design creating many positive outcomes. The use of environmentally friendly materials serves as the key solution, hempcrete used with additives and timber provides a green build design to create the practicality of this proposed passive net zero energy off grid housing unit

The location is placed on a larger design idea based off thesis work. The idea is to create community district that works with than rather fighting with new and old residents, a place for commerce for all. An urban community that has public and private access, welcoming all to the site. To grow the community, spaces such as: a café, crop growing, workspaces, learning rooms, exhibition spaces and social housing—aimed to increase cohesion amongst the community. Further explored in a chance to work on-site to partake in a hempcrete self-build project. People can live on-site and grow their own spaces. The siteservices use traditional and modern strategies to create an off grid industrial processing space.

A place of living for today, tomorrow and many days thereafter . A solution for the new world problem

Sebastian Victor Dawber

1. Location- Function
2. Site- Form
3. Plan. Section , Elevation
4. Detailed Section and Plan
5. Rendered Views

Svdawber@outlook.com
+447393884781

Link to thesis work:


Hackney Wick Fish land social areas


The concept creates a off-grid home for people in the area who are not economically active, this will reduce their living expenses dramatically. Using online data a social analysis was completed to derive the data to create the focus for the users.

The location is in the centre of Hackney Wick London United Kingdom. Close to nearby social locations one does not need to travel far in order to get around.



The 37 sqm space is part of a much larger project with this housing unit being a key part in concept. A space for people to live, work and grow their needed material for the housing project.


The unit is multiplied several times in order to give living spaces for varied users but the housing unit itself is singular in design and implementation.

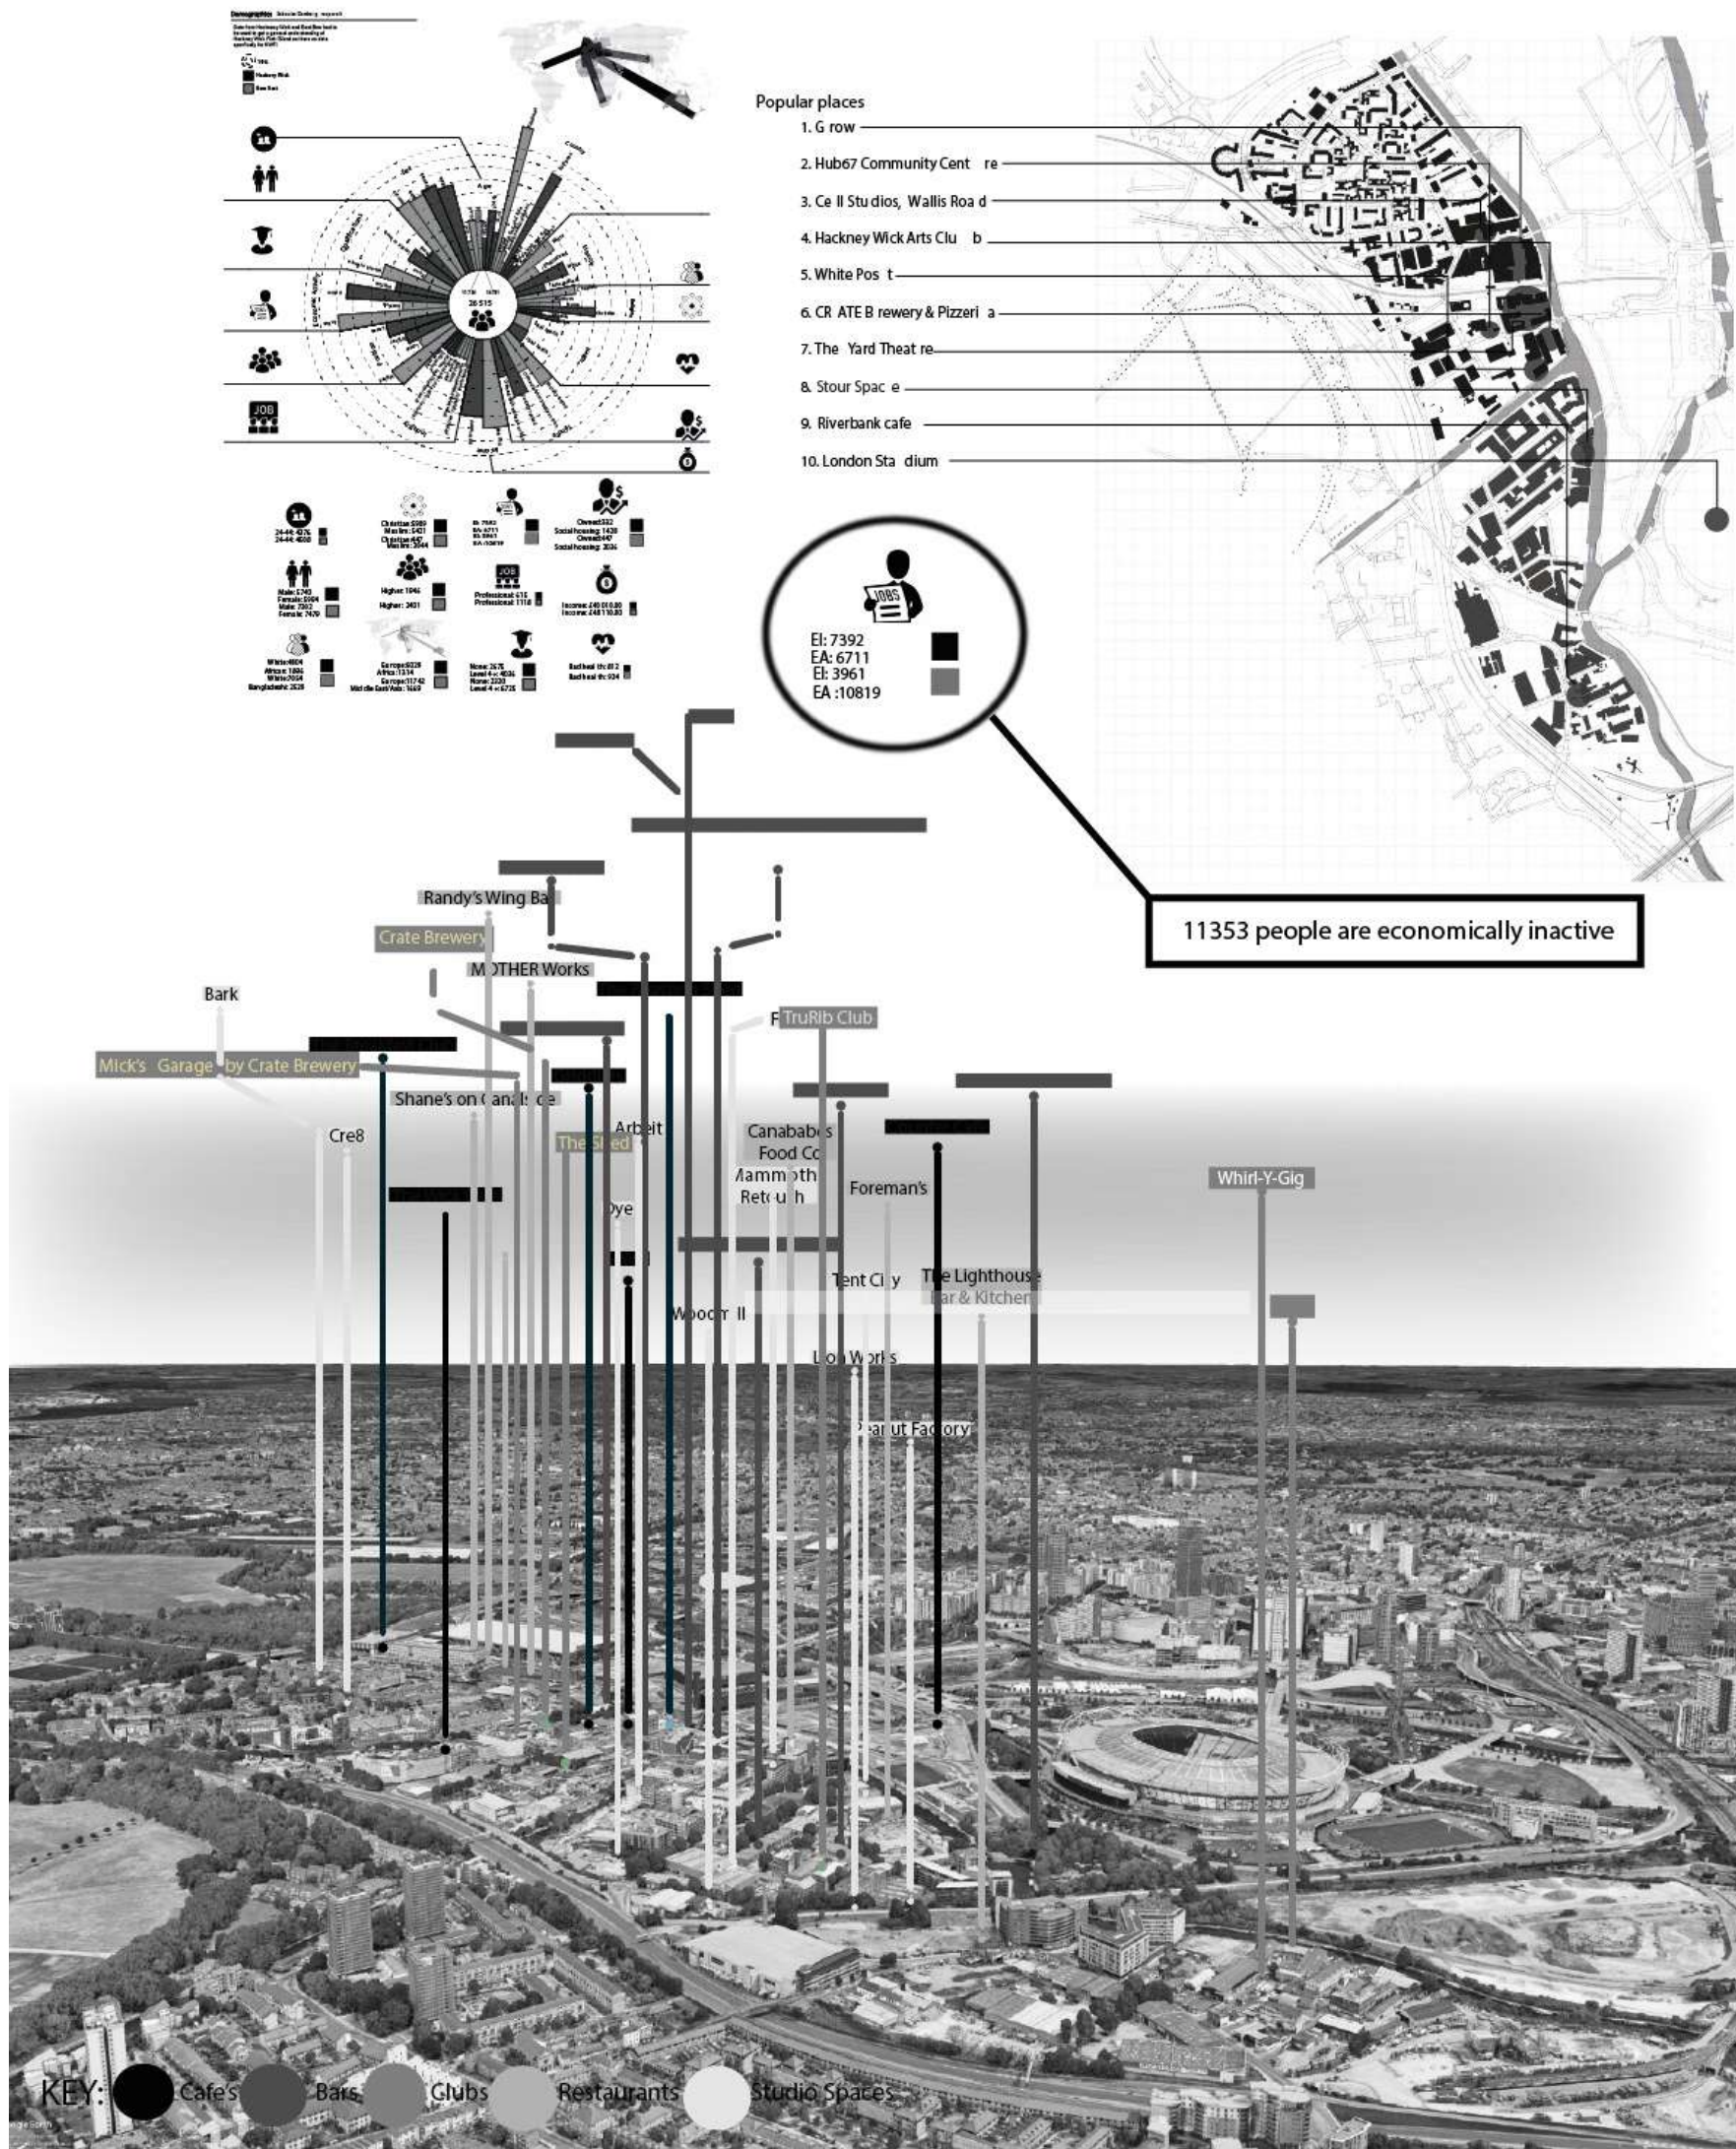


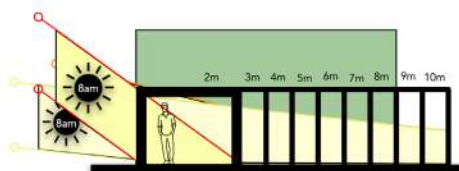


12 pm





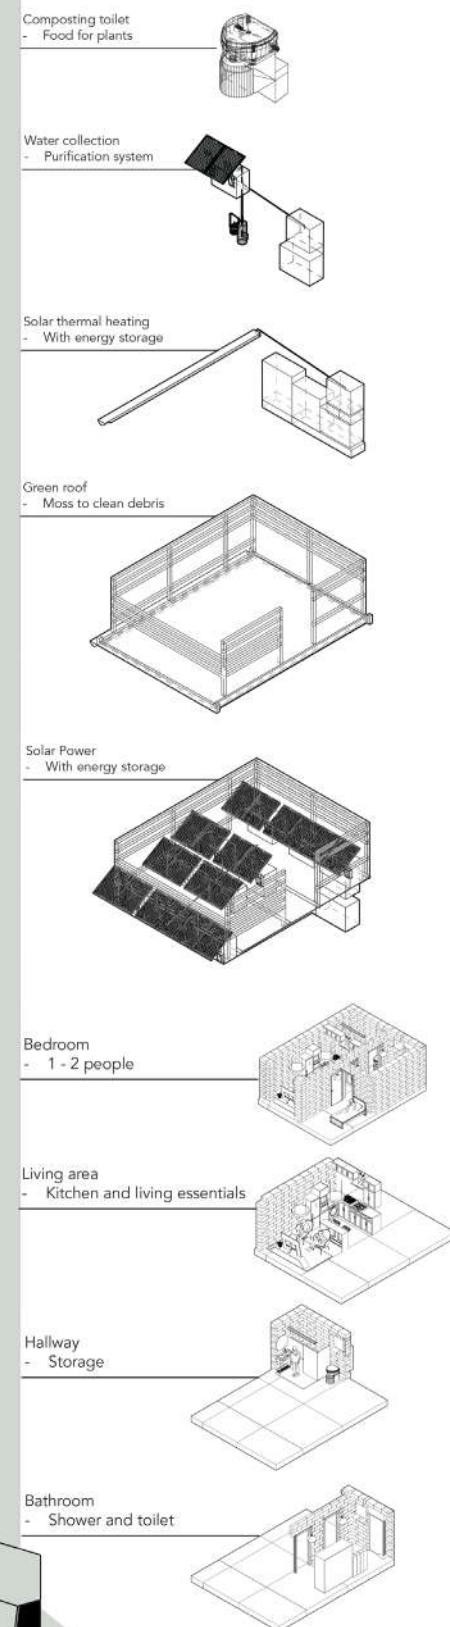
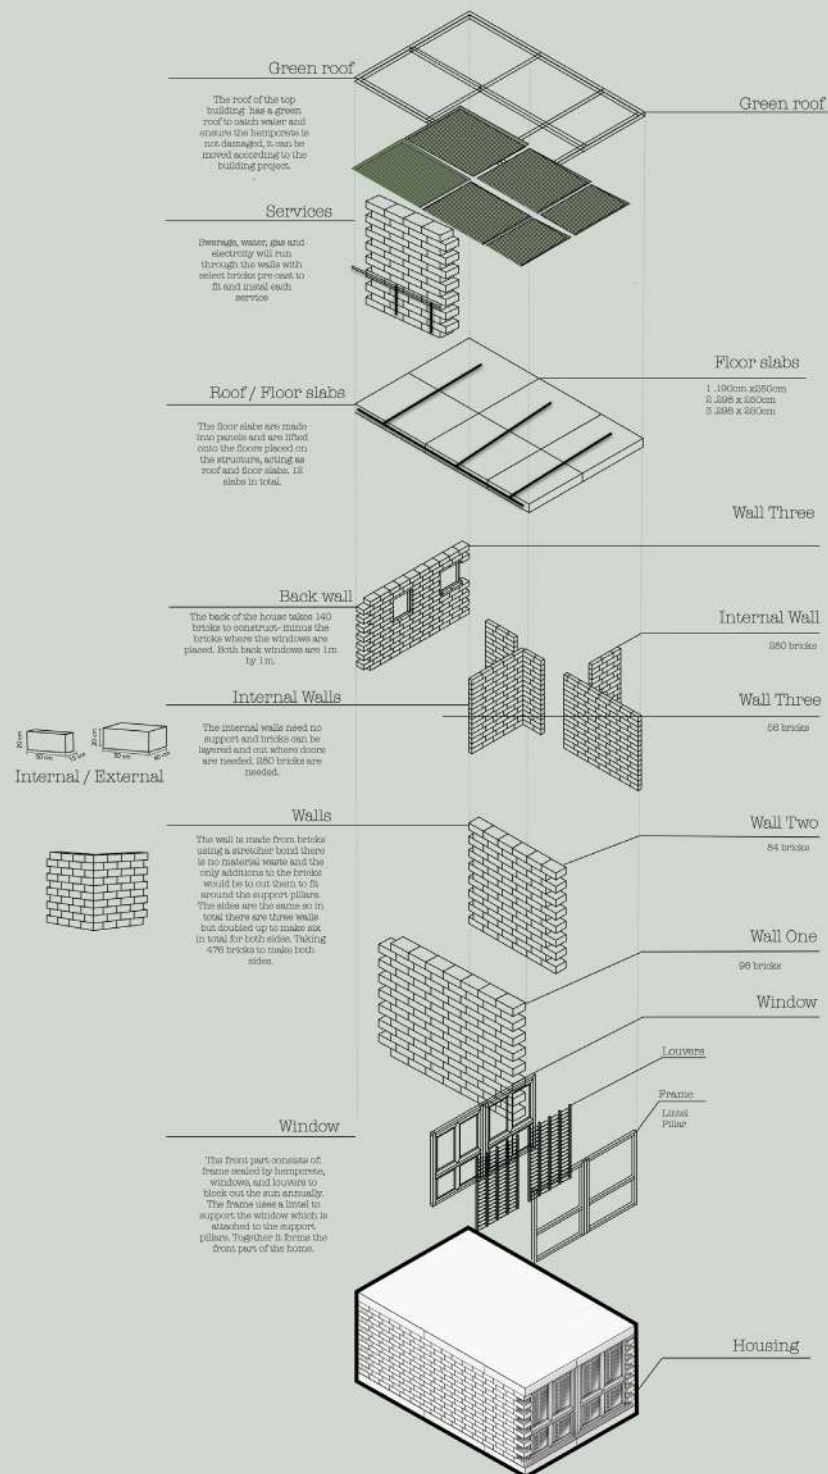


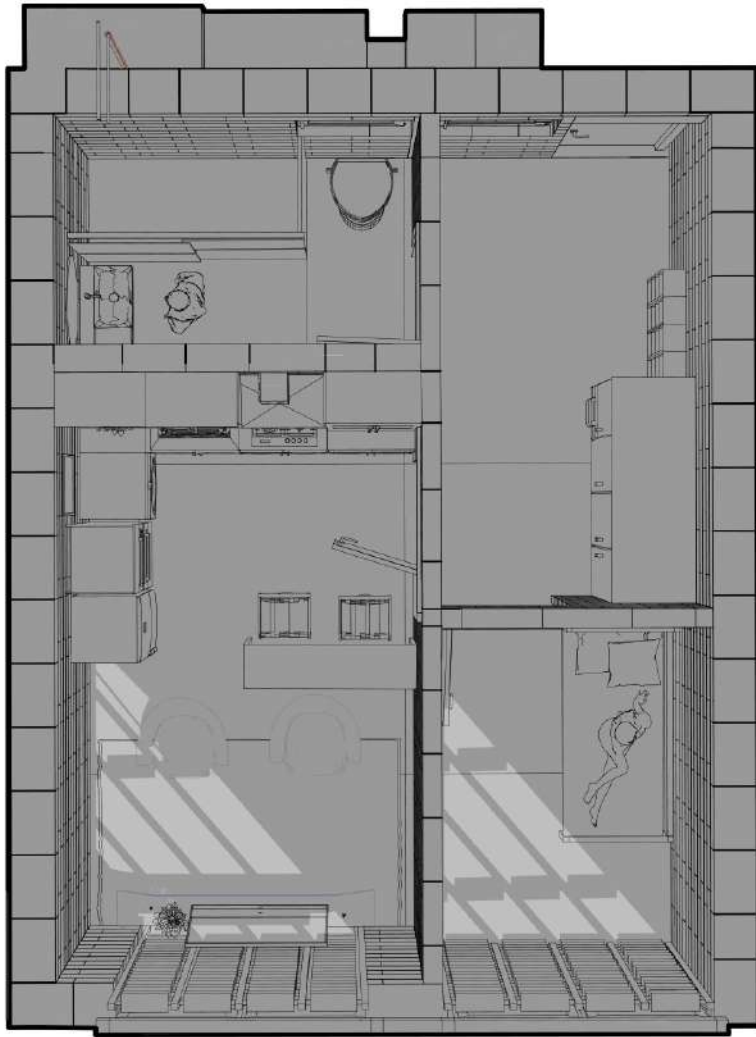

Early wake up then shower with LED lighting to help wake up, the sun kissed eyes from the low lighting helps the brain wake-up naturally

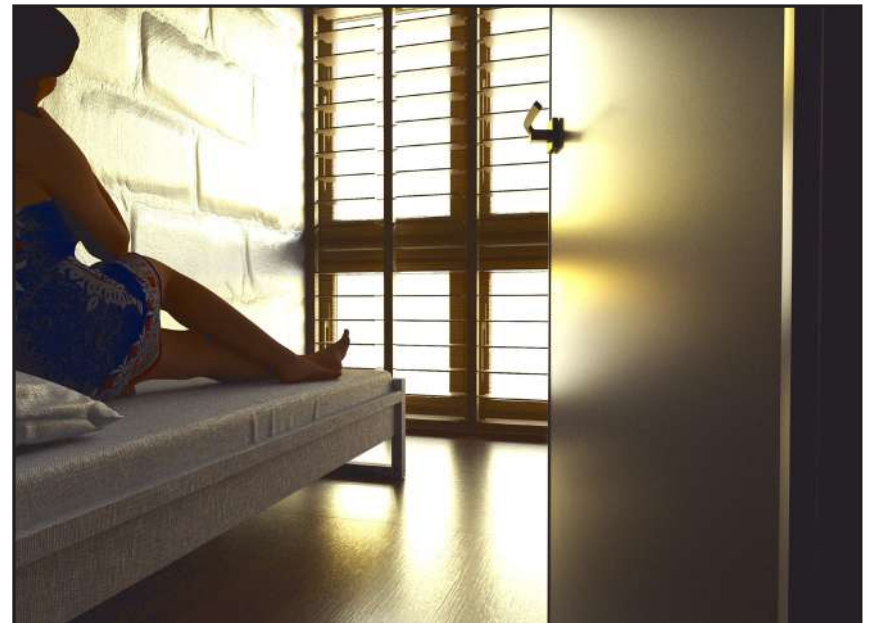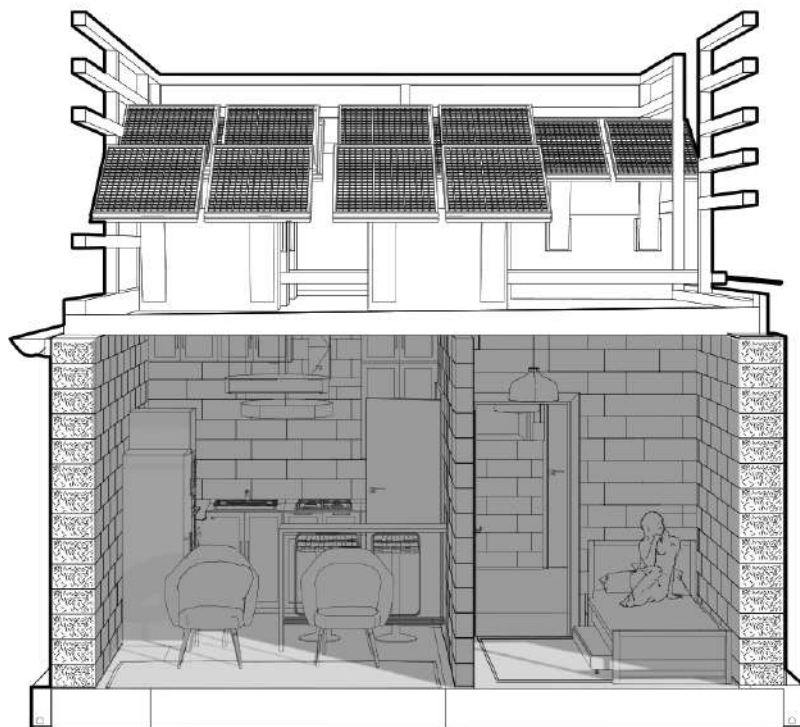

A perfectly curated bedroom to fit a single bed as well as a pull-out for two people. The south facing room with shutters allows for a natural way to start your day

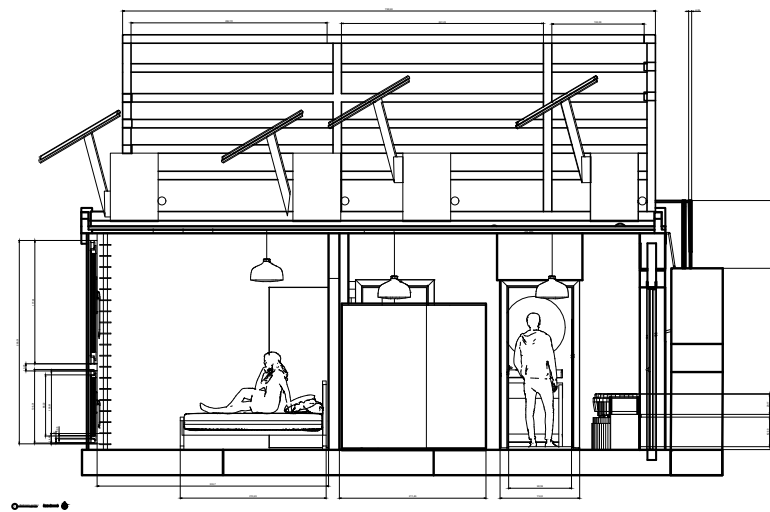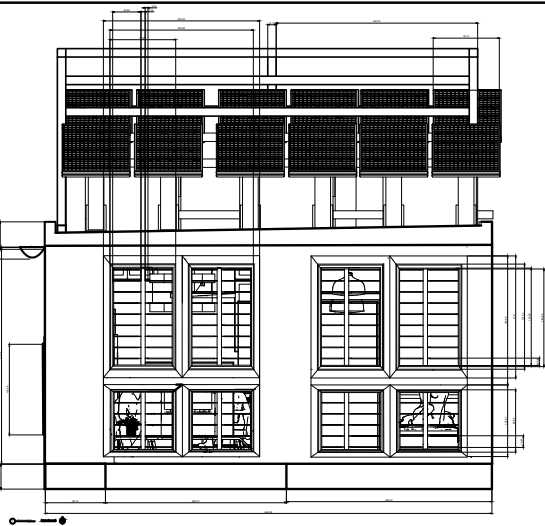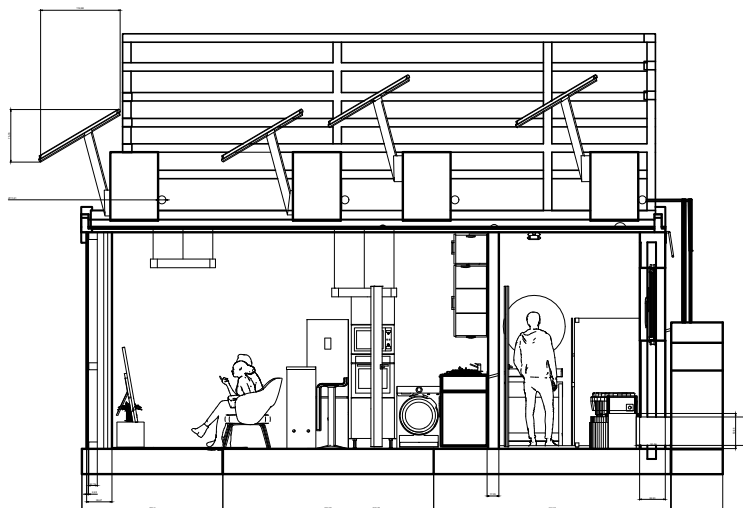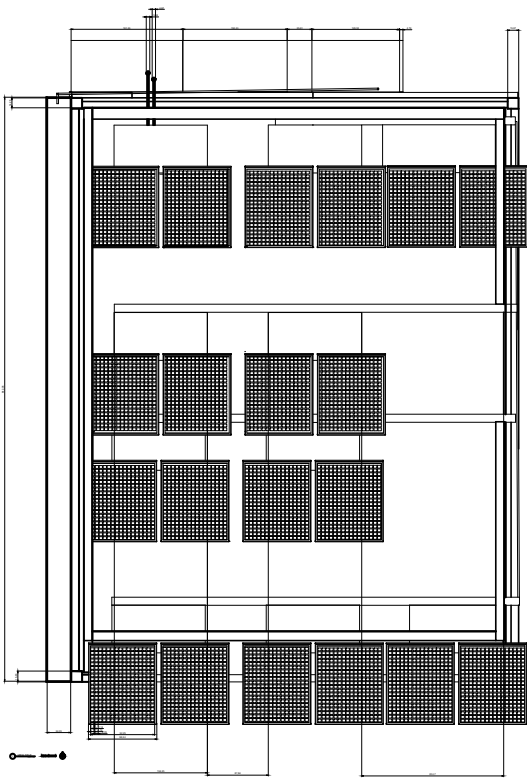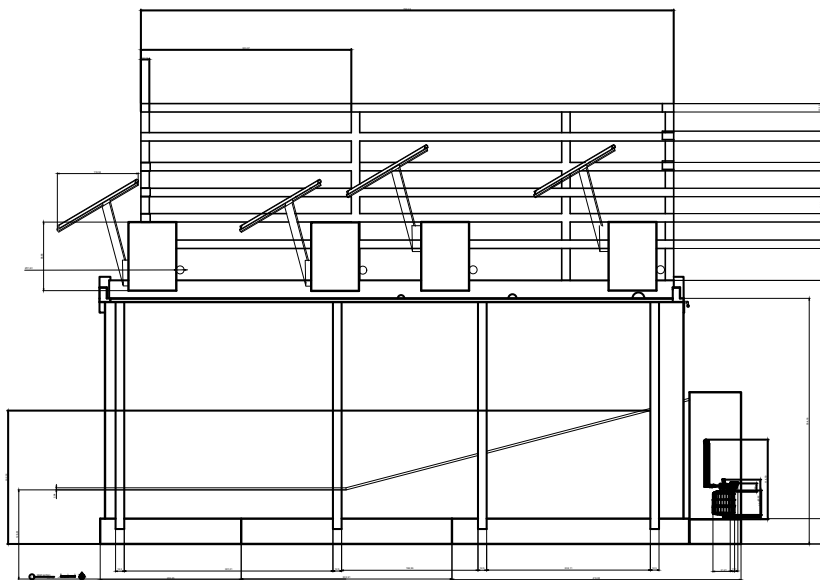
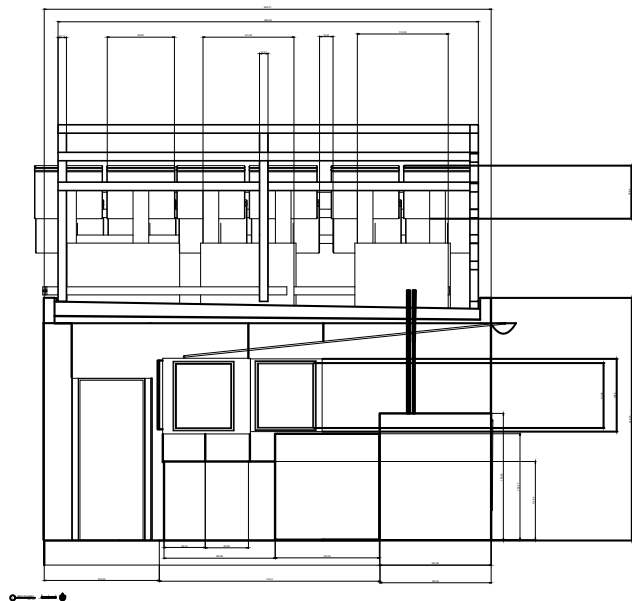


REVISIONS	
REVISIONS	
DRAWING	
Plan / Sections / Elevations	
PROJECT TITLE	
Back to basics	
PRINCIPAL	
Sebastian Victor Dawber Forbidden roots . Ltd.	
PROJECT ADDRESS	
London 1 Hackney Wick	
CAD REF.	DATE
00000001	April 2020
DRAWING No.	SCALE
1	1:100
DRAWN	A
CHECKED	
SV	

Sebastian Victor Dawber

London
Durban

: +44 7770530713
: svdawber@outlook.com
w: website url

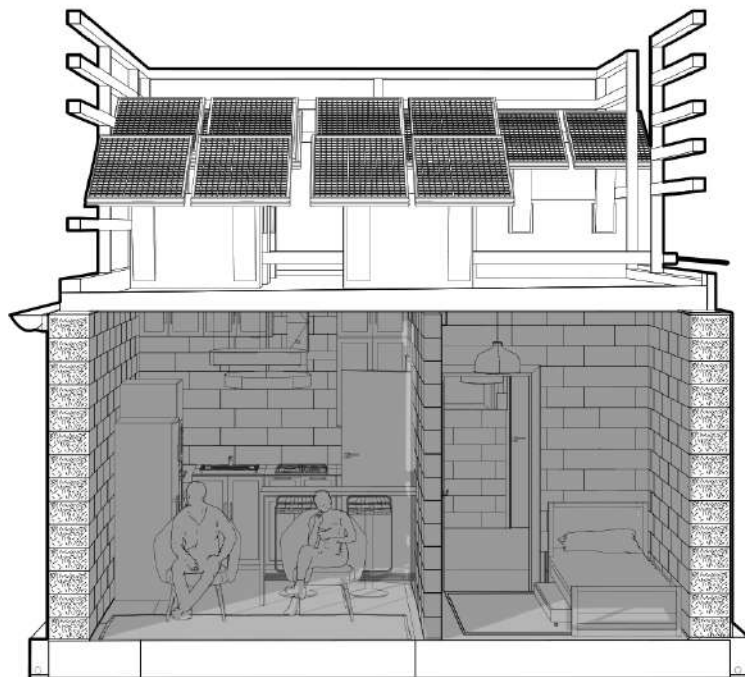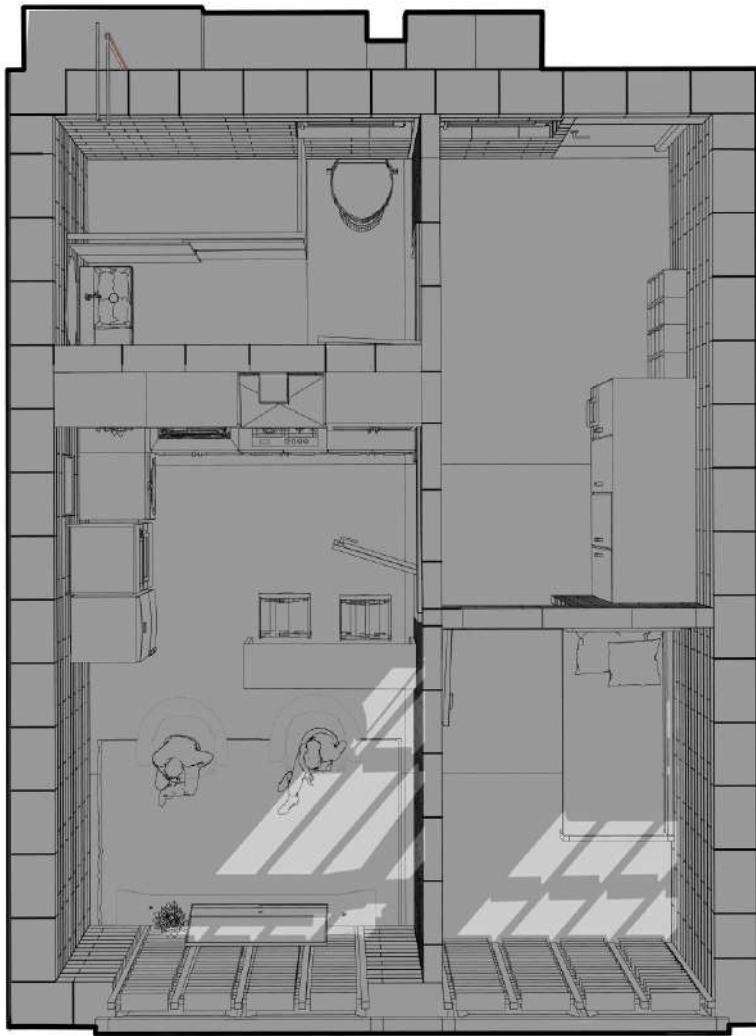

The open plan kitchen and living area offers further environmental control as well as creating a separate space for living.

